



PLAN DE MASSE "Centrale de NOGENT SUR SEINE"

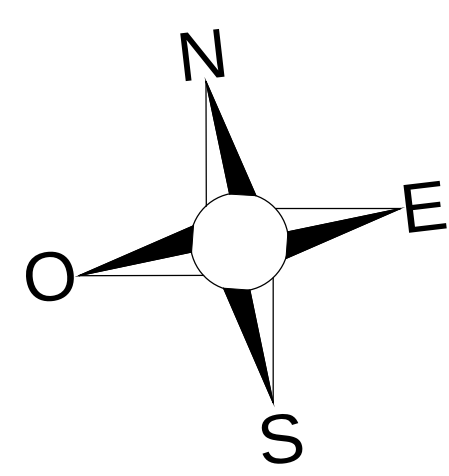

Vers VILLENAUXE

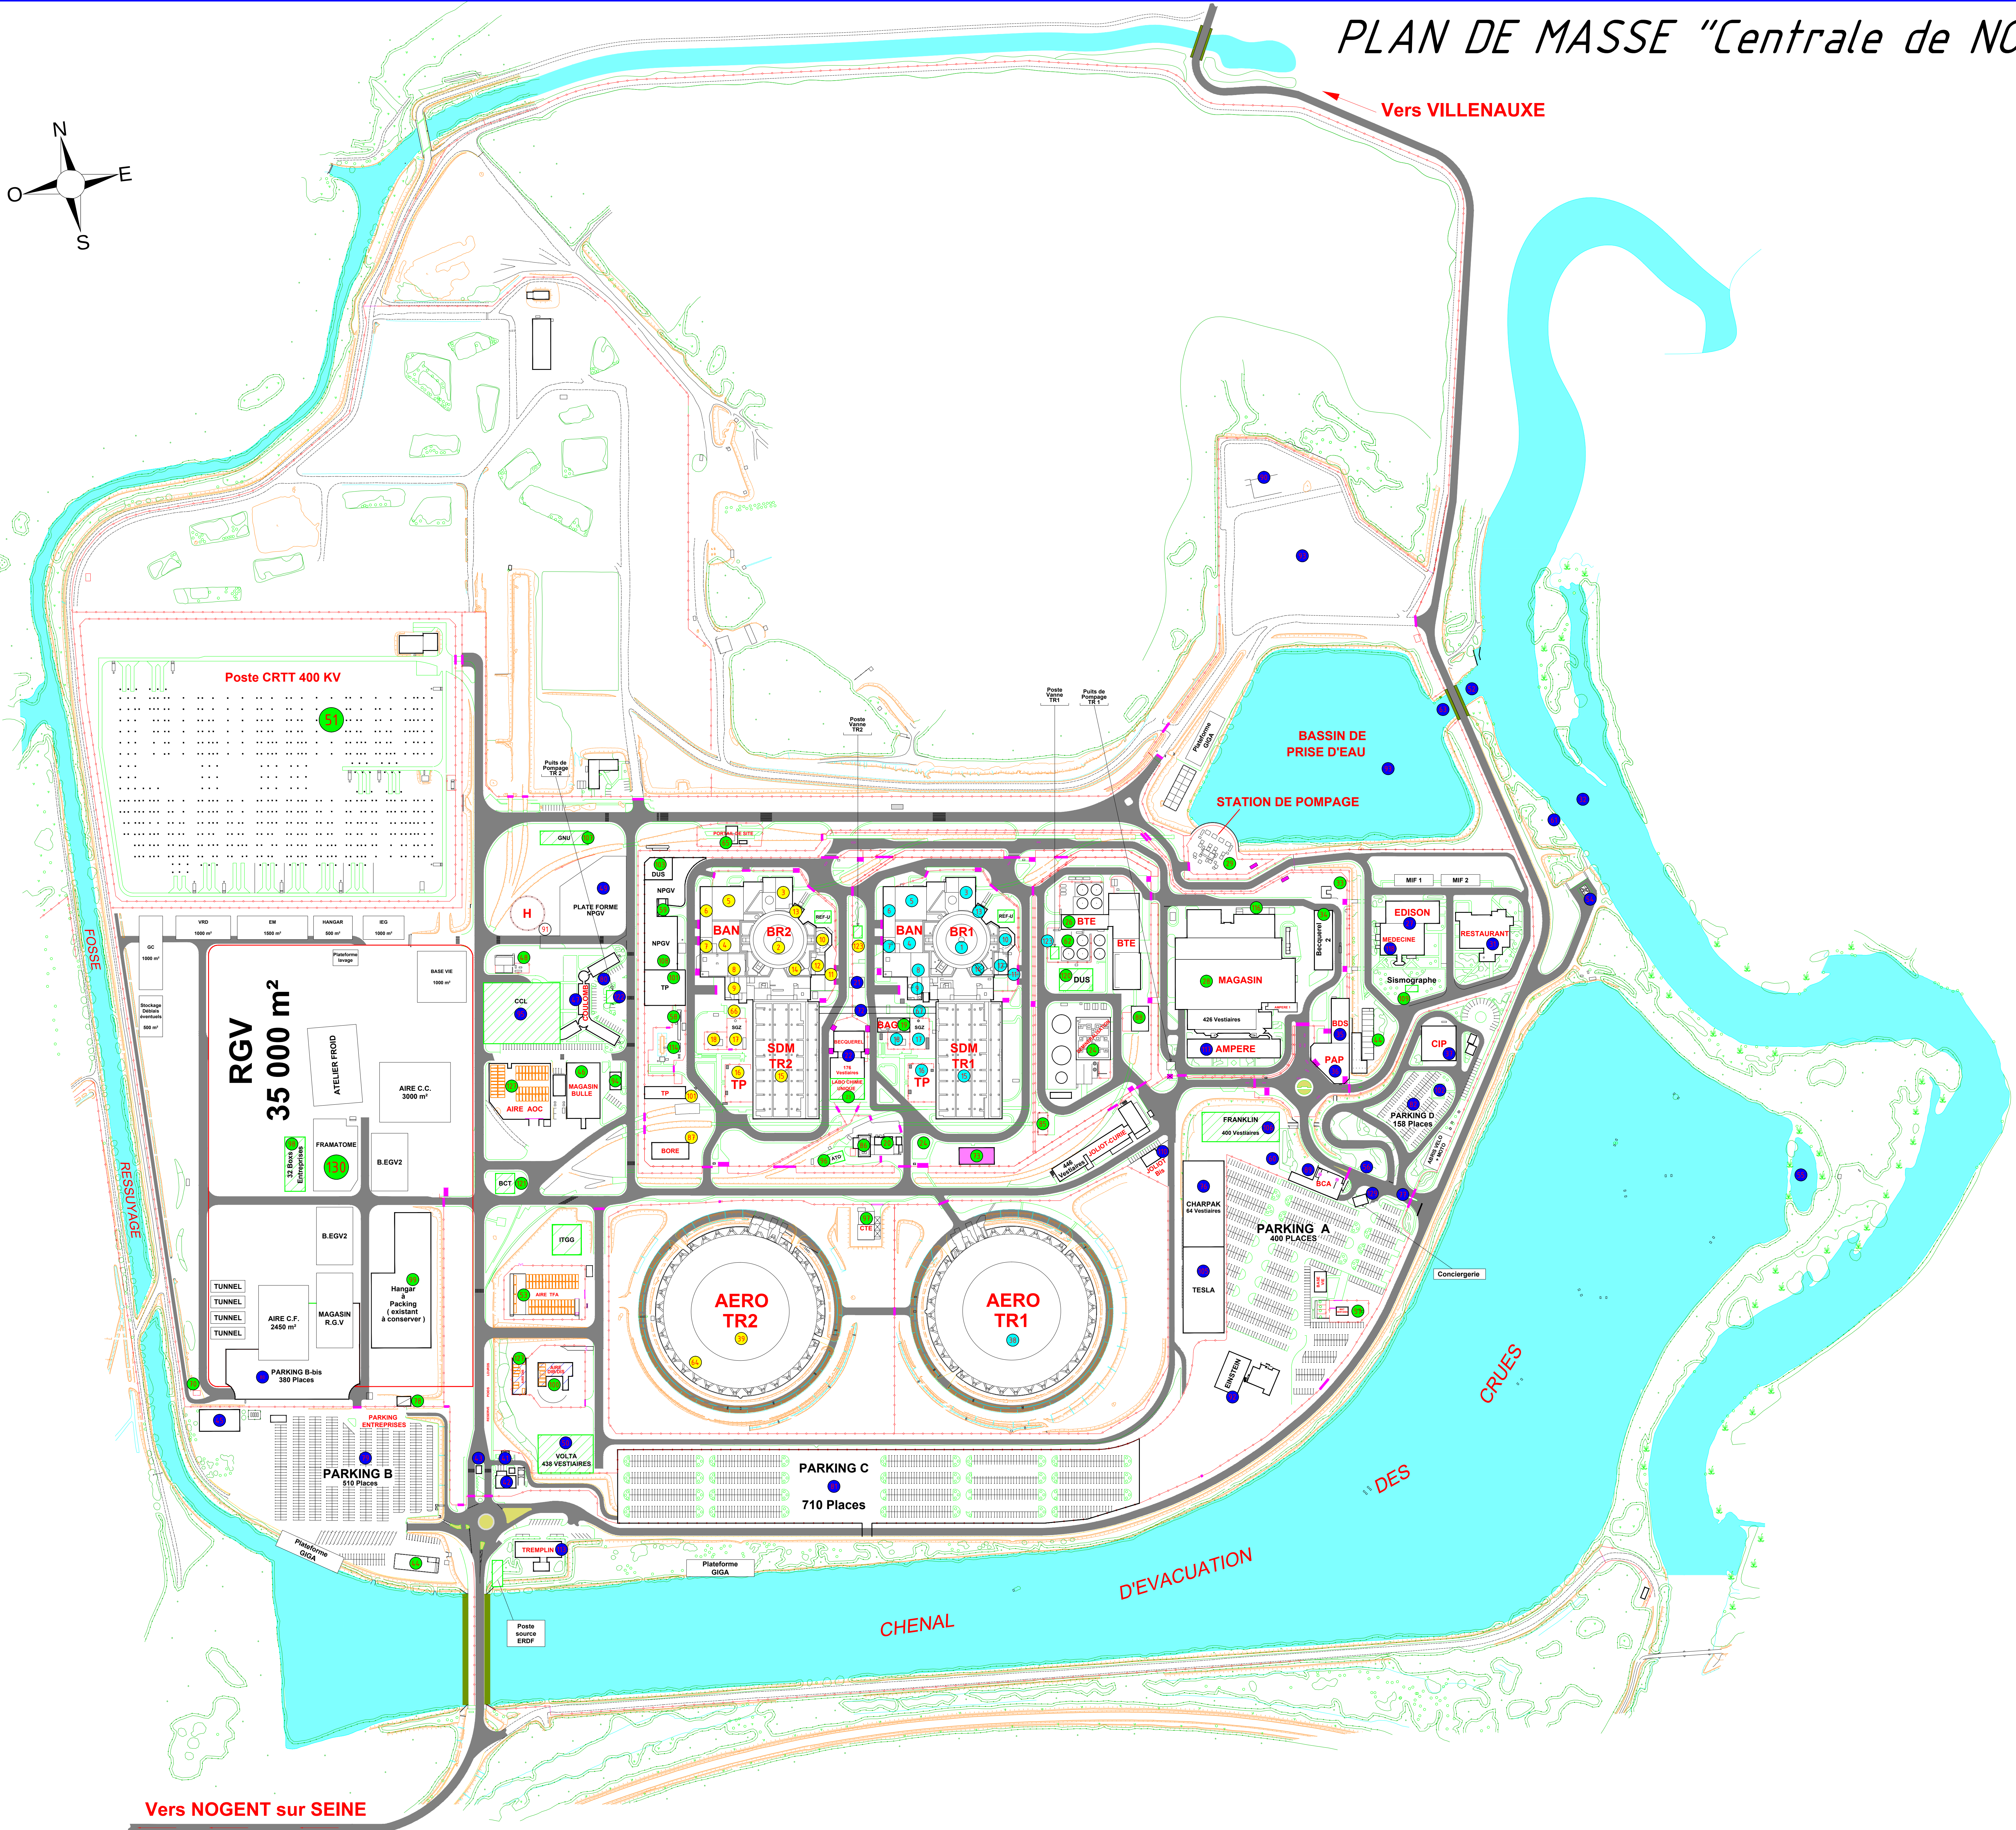

Vers NOGENT sur SEINE

Repère	Désignation du Batiment	Repère	Désignation du Batiment	Repère	Désignation du Batiment
1	BATIMENT REACTEUR 1	66	ARE DE DEPOTAGE OUEST	131	
2	BATIMENT REACTEUR 2	67	ARE DE DEPOTAGE EST	132	
3	BATIMENT COMBUSTIBLE K	68	LOCAL METEO ET MAT ASSOCIE TR3-4	133	
4	BATIMENT DES AUXILIAIRES NUCLEAIRES A (NA)	69	DALLE SODAR	134	
5	B.A.N. B (NB)	70	DALLES STATIONS KRS 1000M	135	
6	B.A.N. C (NC)	71	DALLE PIECE DE RECHANGE TRANSFORMATEURS	136	
7	B.A.N. D (ND)	72	PASSERELLE SUC - SOM	137	
8	BATIMENT D'EXPLOITATION (W)	73	LOCAL VACCINATION ET AIRE DE DEPOTAGE ASSOCIEE	138	
9	BATIMENT ELECTROGENE voie A	74		139	
10	RESERVOIR PTR	75	TOUR D'ACCES	140	
11	BACHE A FUEL	76	CHARPAK		
12	BATIMENT ELECTROGENE voie B	77	ENTREE PARKING A		
13	PORTIQUE DE MANUTENTION	78	MAGASIN RELAIS		
14	BATIMENT ELECTRIQUE (BL BAS)	79	PARKING B		
15	SALLE DES MACHINES	80	PARKING B-bis		
16	TRANSFORMATEUR PRINCIPAL	81	PARKING C		
17	PLATEFORME STOCKAGE H2 ET H2	82	PARKING D		
18	TRANSFORMATEUR AUXILIAIRE	83	LOCALS PRODUITS CHIMIQUES DANGEREUX		
19	BATIMENT DES AUXILIAIRES GENERAUX (BAI)	84	LOCALS DEPOT GAZ		
20	OUVRAGE D'APPOINT	85	DALLE DE STOCKAGE DES FUTS VIDES		
21	BCE BATIMENT CONDUITE EXPLOITATION	86	TRAITEMENT AEROREFRIGERANTS (ICF)		
22	BATIMENT RECOVEREL - CHANTIER ECOLE	87	BATIMENT BORE		
23	LABO CHIMIE UNIQUE	88	LABORATOIRE AMBE (IP3)		
24	PYLONE D'EVACUATION D'ENERGIE	89	BATIMENT DE CONTRÔLE D'ACCES (BES)		
25	STATION DE DEMINERALISATION	90	BASSIN DE DECANTATION		
26	BATIMENT DE TRAITEMENT DES EFFLUENTS BTE A B C	91	HELISURFACE		
27	THOMAS EDISON	92	EINSTEIN		
28	BATIMENT AMPERE - MAGASIN GENERAL	93	BASSIN DE PRISE D'EAU		
29	STATION DE POMPAGE	94	GARAGE AMENAGEMENT		
30	BASSIN DE DESHULAGE RESEAU SEO	95	CCL		
31	RESTAURANT DE SITE	96	LOCAL ATD		
32	OUVRAGE DE REJET	97	CTE TR1/TR2 (PAIRE DE TRANCHE)		
33	OUVRAGE DE MELANGE	98	32 BOXS ENTREPRISES		
34	AIRE GRILLAGEE	99	HANGAR A PACKING		
35	BLOC DE SECURITE BDS	100	DECHETTERIE AIRE DIB/DIS		
36	POSTE D'ACCES PRINCIPAL PAP	101	PLATEFORME TRANSFO - TP		
37	CENTRE D'INFORMATION AU PUBLIC CIP	102	MUSEE PWR		
38	REFRIGERANT ATMOSPHERIQUE TR1	103	BATIMENT DUS TR1 Option B		
39	REFRIGERANT ATMOSPHERIQUE TR2	104	BATIMENT JOLIOT CURIE - AT - PMER - PRESTATAIRES - VESTIAIRES		
40		105	CHARPAK		
41	LOCAL PIT	106	FRANKLIN		
42	POSTE DE GARDE (BES N°2)	107	PARC A GAZ GNU		
43	PAS Vehicule	108	NPGV		
44	BASSIN D'ORAGE DESHUIEUR RESEAU SEO	109	SISMOGRAPHIE		
45	Salle de musculation + AE	110	JOLIOT CURIE BIS		
46	MAGASIN BULLE	111	VESTIAIRES ENTREPRISES		
47	BATIMENT CHARLES COULOMB	112	TREPLIN		
48	POSTE ELECTRIQUE	113			
49	PLATE FORME NP/GV	114	GROUPE ELECTROGENE DE SECOURS		
50	VOLTA 438 VESTIAIRES	115			
51	POSTE CRIT 400KV	116	AIRE GRILLAGEE		
52	DROME	117	ANDRE AMPERE		
53	AIRE TFA	118	SERVICE DE SANTE AU TRAVAIL		
54	OUVRAGE DISOLEMENT	119	ASG		
55	ZONE DE DEVELOPPEMENT ORNITHOLOGIQUE	120	BATIMENT DUS TR1 Option C		
56	GARE ROUTIERE	121	BCT		
57	BATIMENT FAISCEAU HERTZIEN	122	PUITS DE POMPAGE DE NAPPE TR2		
58	TURBINE A COMBUSTION (TAC)	123	POSTE VANNE TR1		
59	BATIMENT DE SUPPRESSION	124	POSTE VANNE TR2		
60	GARAGE A VELOS	125	PILLIER NON CONTRACTUELS DU REFERENTIEL GEODESIQUE DU SITE		
61	STATION DE PRELEVEMENT D'EAU	126	PILLIER CONTRACTUELS DU REFERENTIEL GEODESIQUE DU SITE		
62	RESERVOIRS KER TER SEK	127	AIRE AOC		
63	OUVRAGE DE PRISE	128	BUREAU SECURITE		
64	LOCAL MESURES REFRIGERANT 2	129	CONCIERGE		
65	PORTIQUE DE MANUTENTION DMK	130	FRAMATOME		

- Implantations Validées
- Projets d'implantations
- Démolitions prévus ou réalisés

0503/01/18ORYAGARNIERCAEMISE A JOUR - AJOUT NOUVEAU BATIMENTS

0430/01/12OCEAWALLONCAEDOSSIER PNPP 3209 ET PNPP 3118

0319/03/10RISYSWALLONCAEMISE A JOUR APPELATION DES BATIMENTS

INDICE

DATE

DESSINE PAR

VERIFIE PAR

ETAT

MODIFICATIONS

OBSERVATIONS

CONTROLE PAR

EDF

Nogent sur seine

CODE EDF

PNO AM100 - 00

INDICES

030405

ECHELLE

1/2000

FORMAT

A0

PLAN DE MASSE

DU CNPE DE NOGENT SUR SEINE